

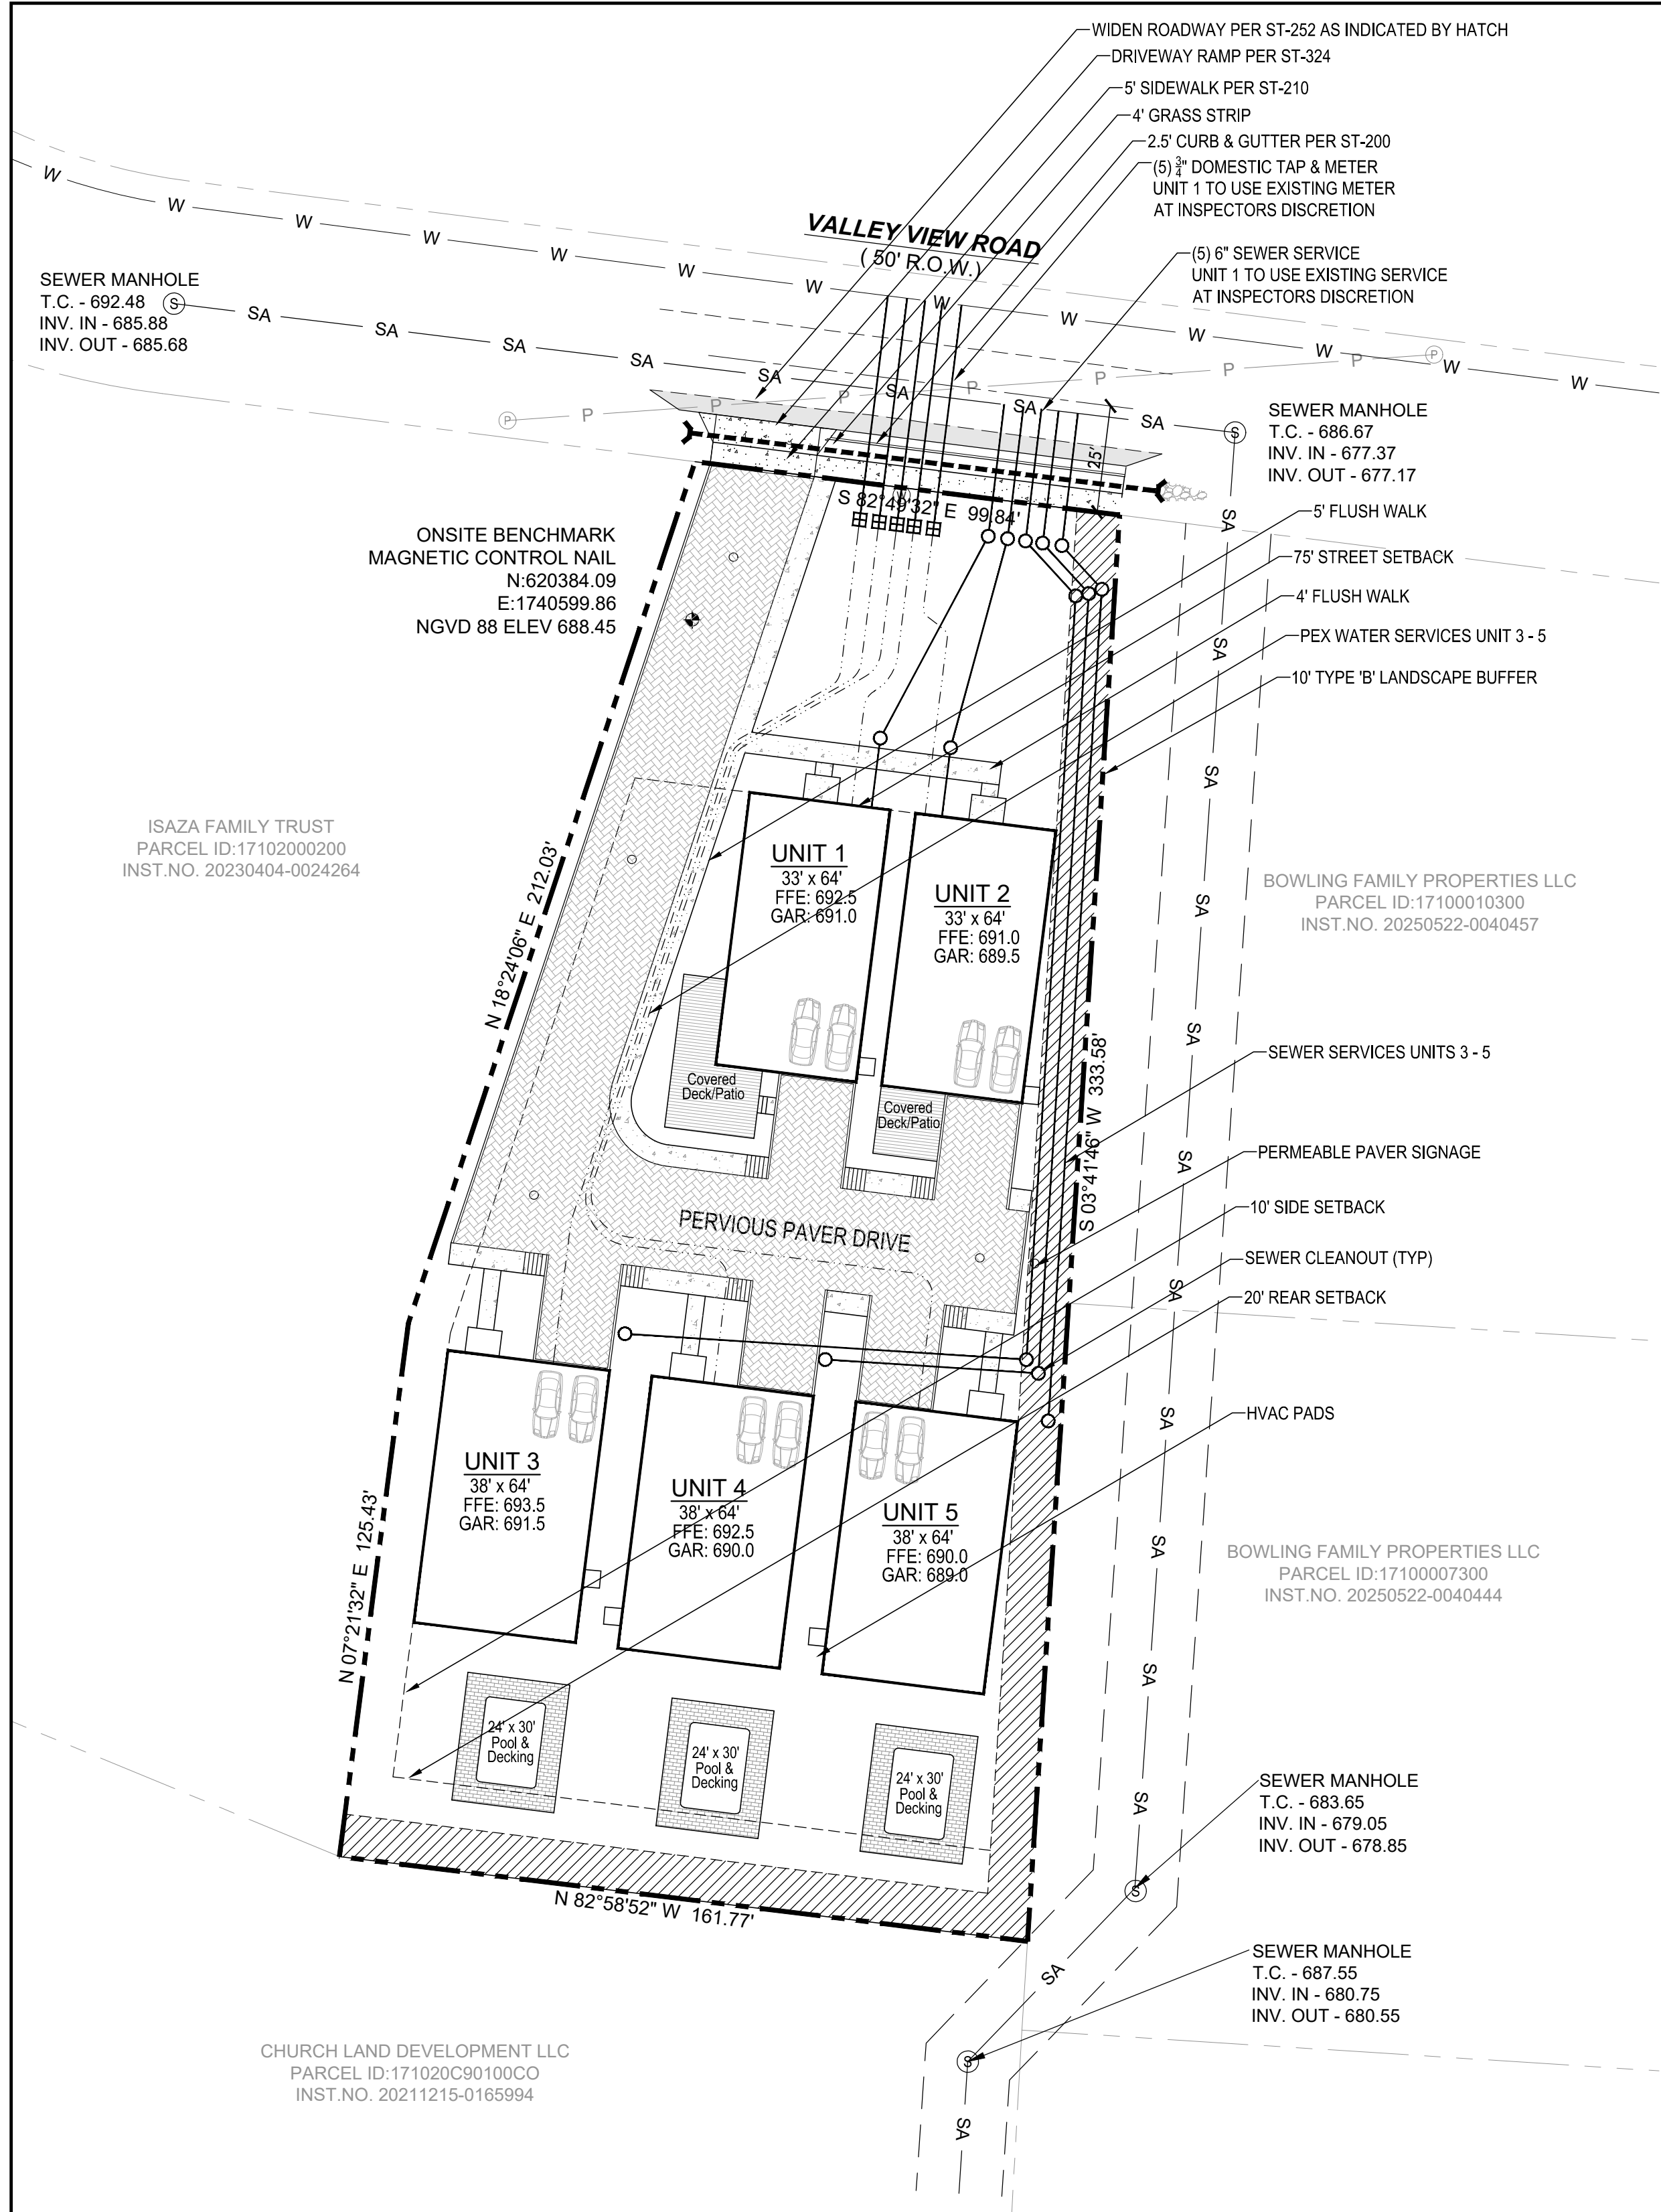
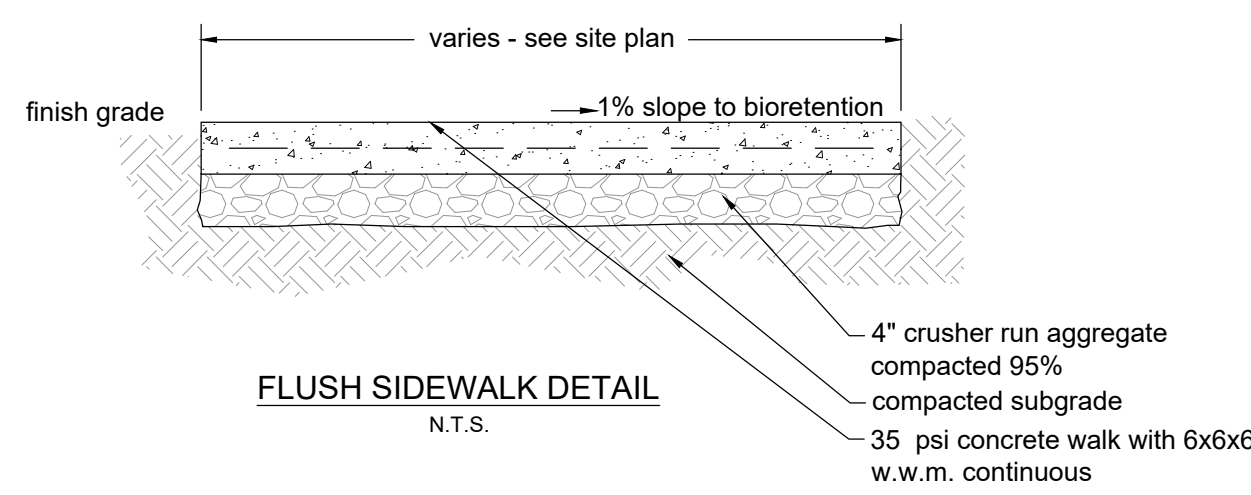
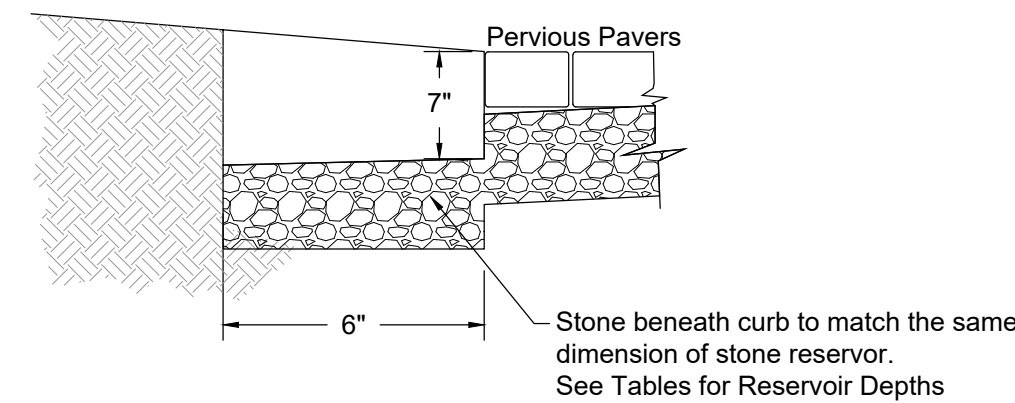
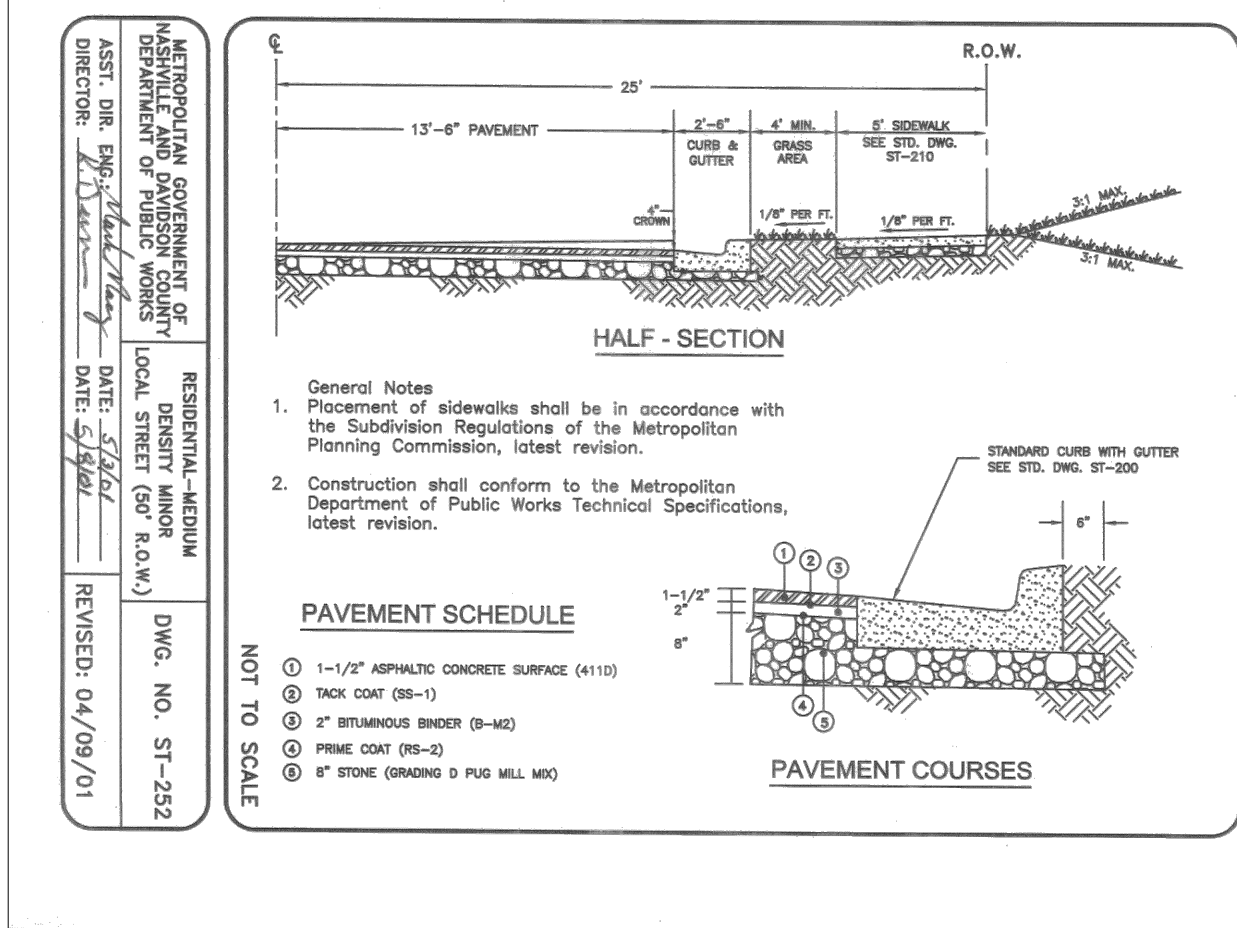
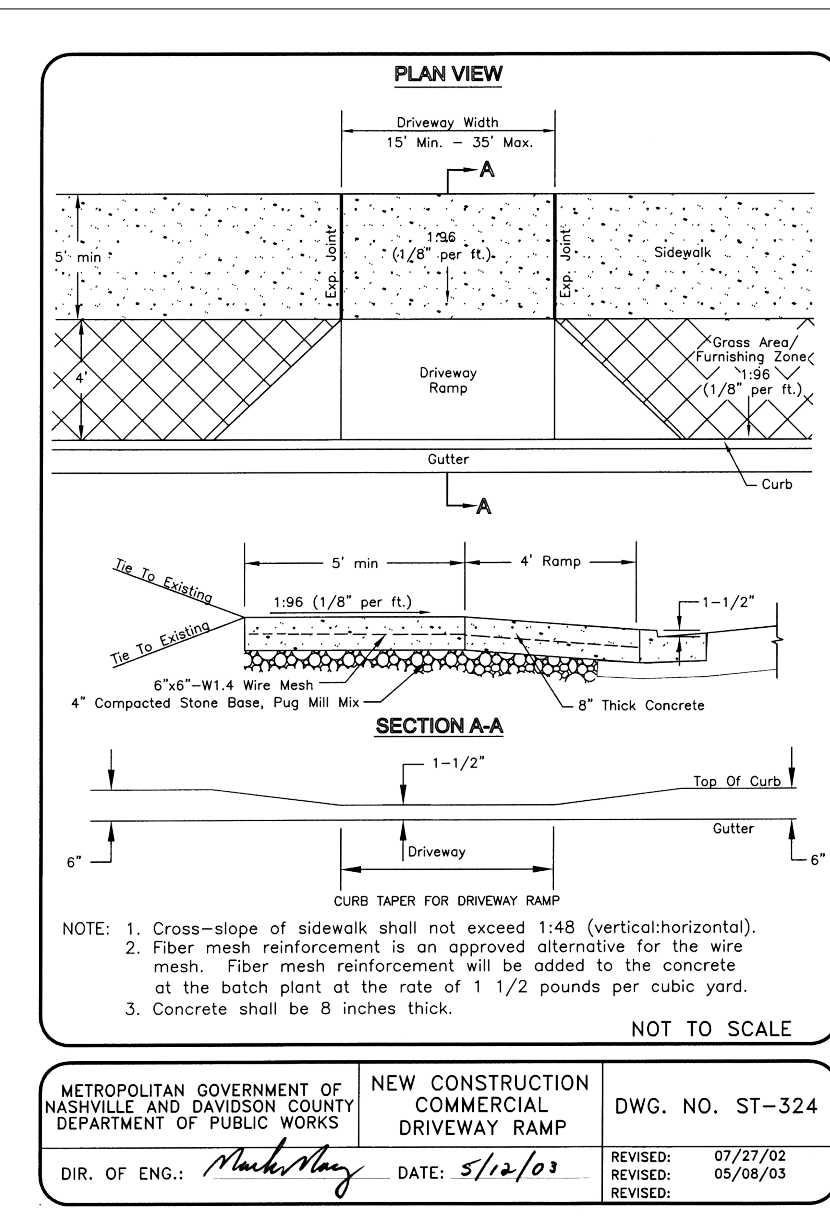


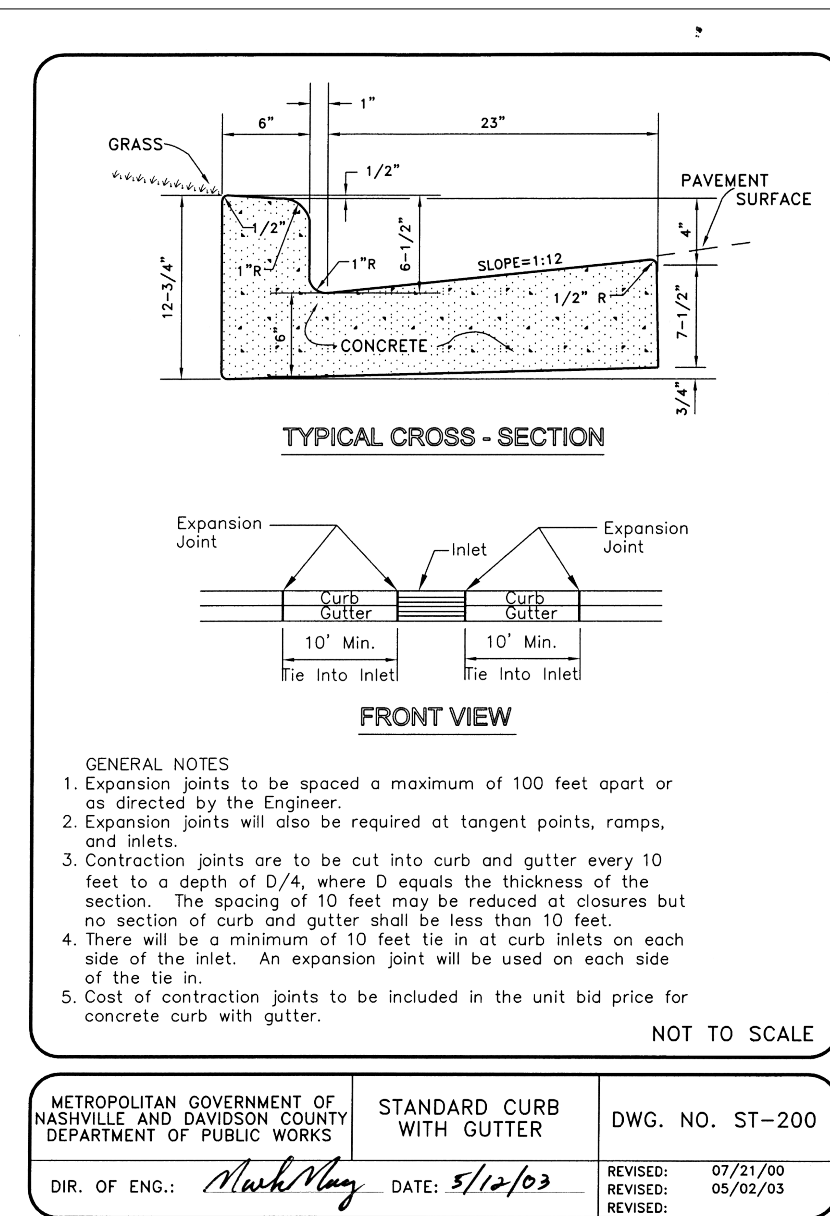

MWS Standard Private Utility Plan Notes

- All water and sewer construction shall be in accordance with specifications and standard details of the metro Water Services.
- All connections to existing manholes shall be by coring and resilient connector method.
- Vertical Double Check Valve Assemblies, that are located in interior rooms, can only be used for fire services.
- All water meters shall be a minimum of 24" not to exceed a maximum of 28" below finished grade.
- Irrigation line shall be copper from the meter to the backflow preventer.
- The minimum fees outlined in the capacity letter must be paid before commercial construction plans can be reviewed.
- All sewer services shall be minimum 6 inches in diameter, from connection at the main until the fires clean out assembly.
- Backflow device to remain accessible at all times.
- Plan size shall be 24" x 36" and shall show contours around meter boxes.
- Any unused existing water meters must be cut and capped at the public main.
- All lead or galvanized water service lines encountered with the project shall be reinstated with copper of like size from the water main to the meter box.
- Domestic and irrigation water meters and associated appurtenances shall be placed in or under a paved or improved surface other than the portion of the service located within the right of way.
- Sanitary sewer taps shall be placed at the lowest adjacent sewer main elevation for each premises and shall not be located in or under a paved or improved surface other than the portion within the right of way.

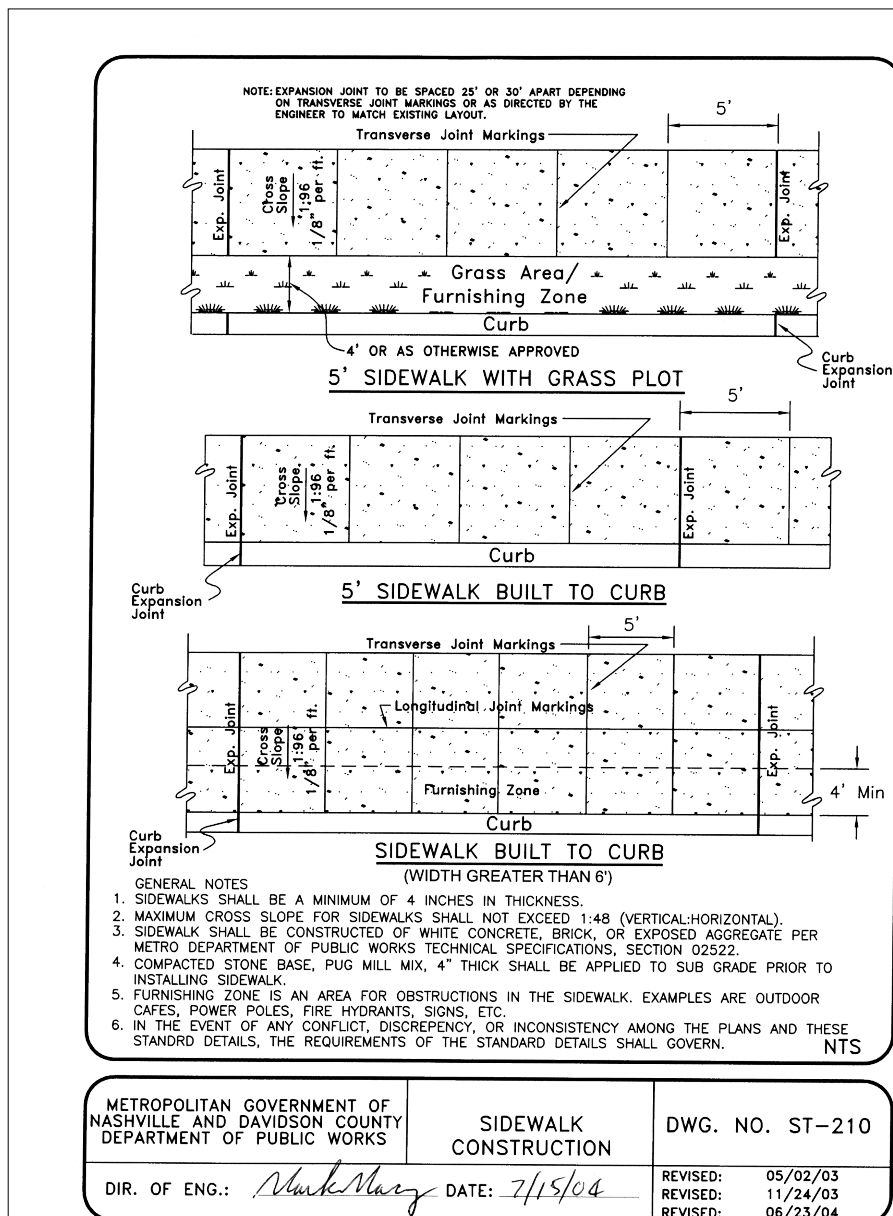


Solid Waste Notes

Trash & Recycling Pick up to be provided by private hauler.

Individual Roll-away cans shall be utilized for pick up.

Contract with private hauler shall be provided prior to Building Permit issuance.

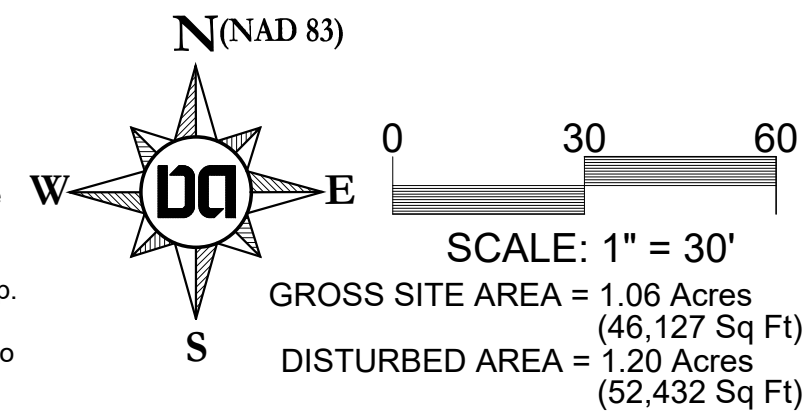

Permits	
MPC Case No	2024SP-039-002
SWGR	2025095494
MWS (Sewer)	2025-----

Dale & Associates
Civil Engineering
Land Planning & Zoning
Surveying


D&A Project #25095
Brentwood Chase 3
5655 Valley View

C1.0

Final SP

5655 Valley View

Parcel 74 on Tax Map 171
Brentwood, Davidson County, Tennessee

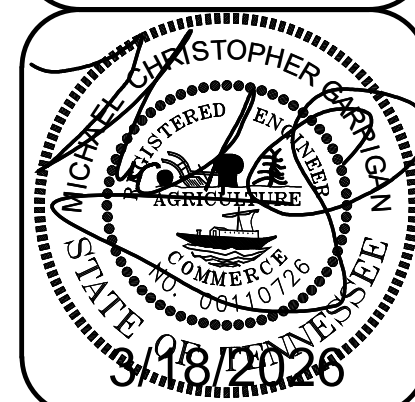

Site Layout &
Utility Plan